
LOFT KAT — YATAK / BANYO / JAKUZİ YERLEŞİM ÖNERİSİ

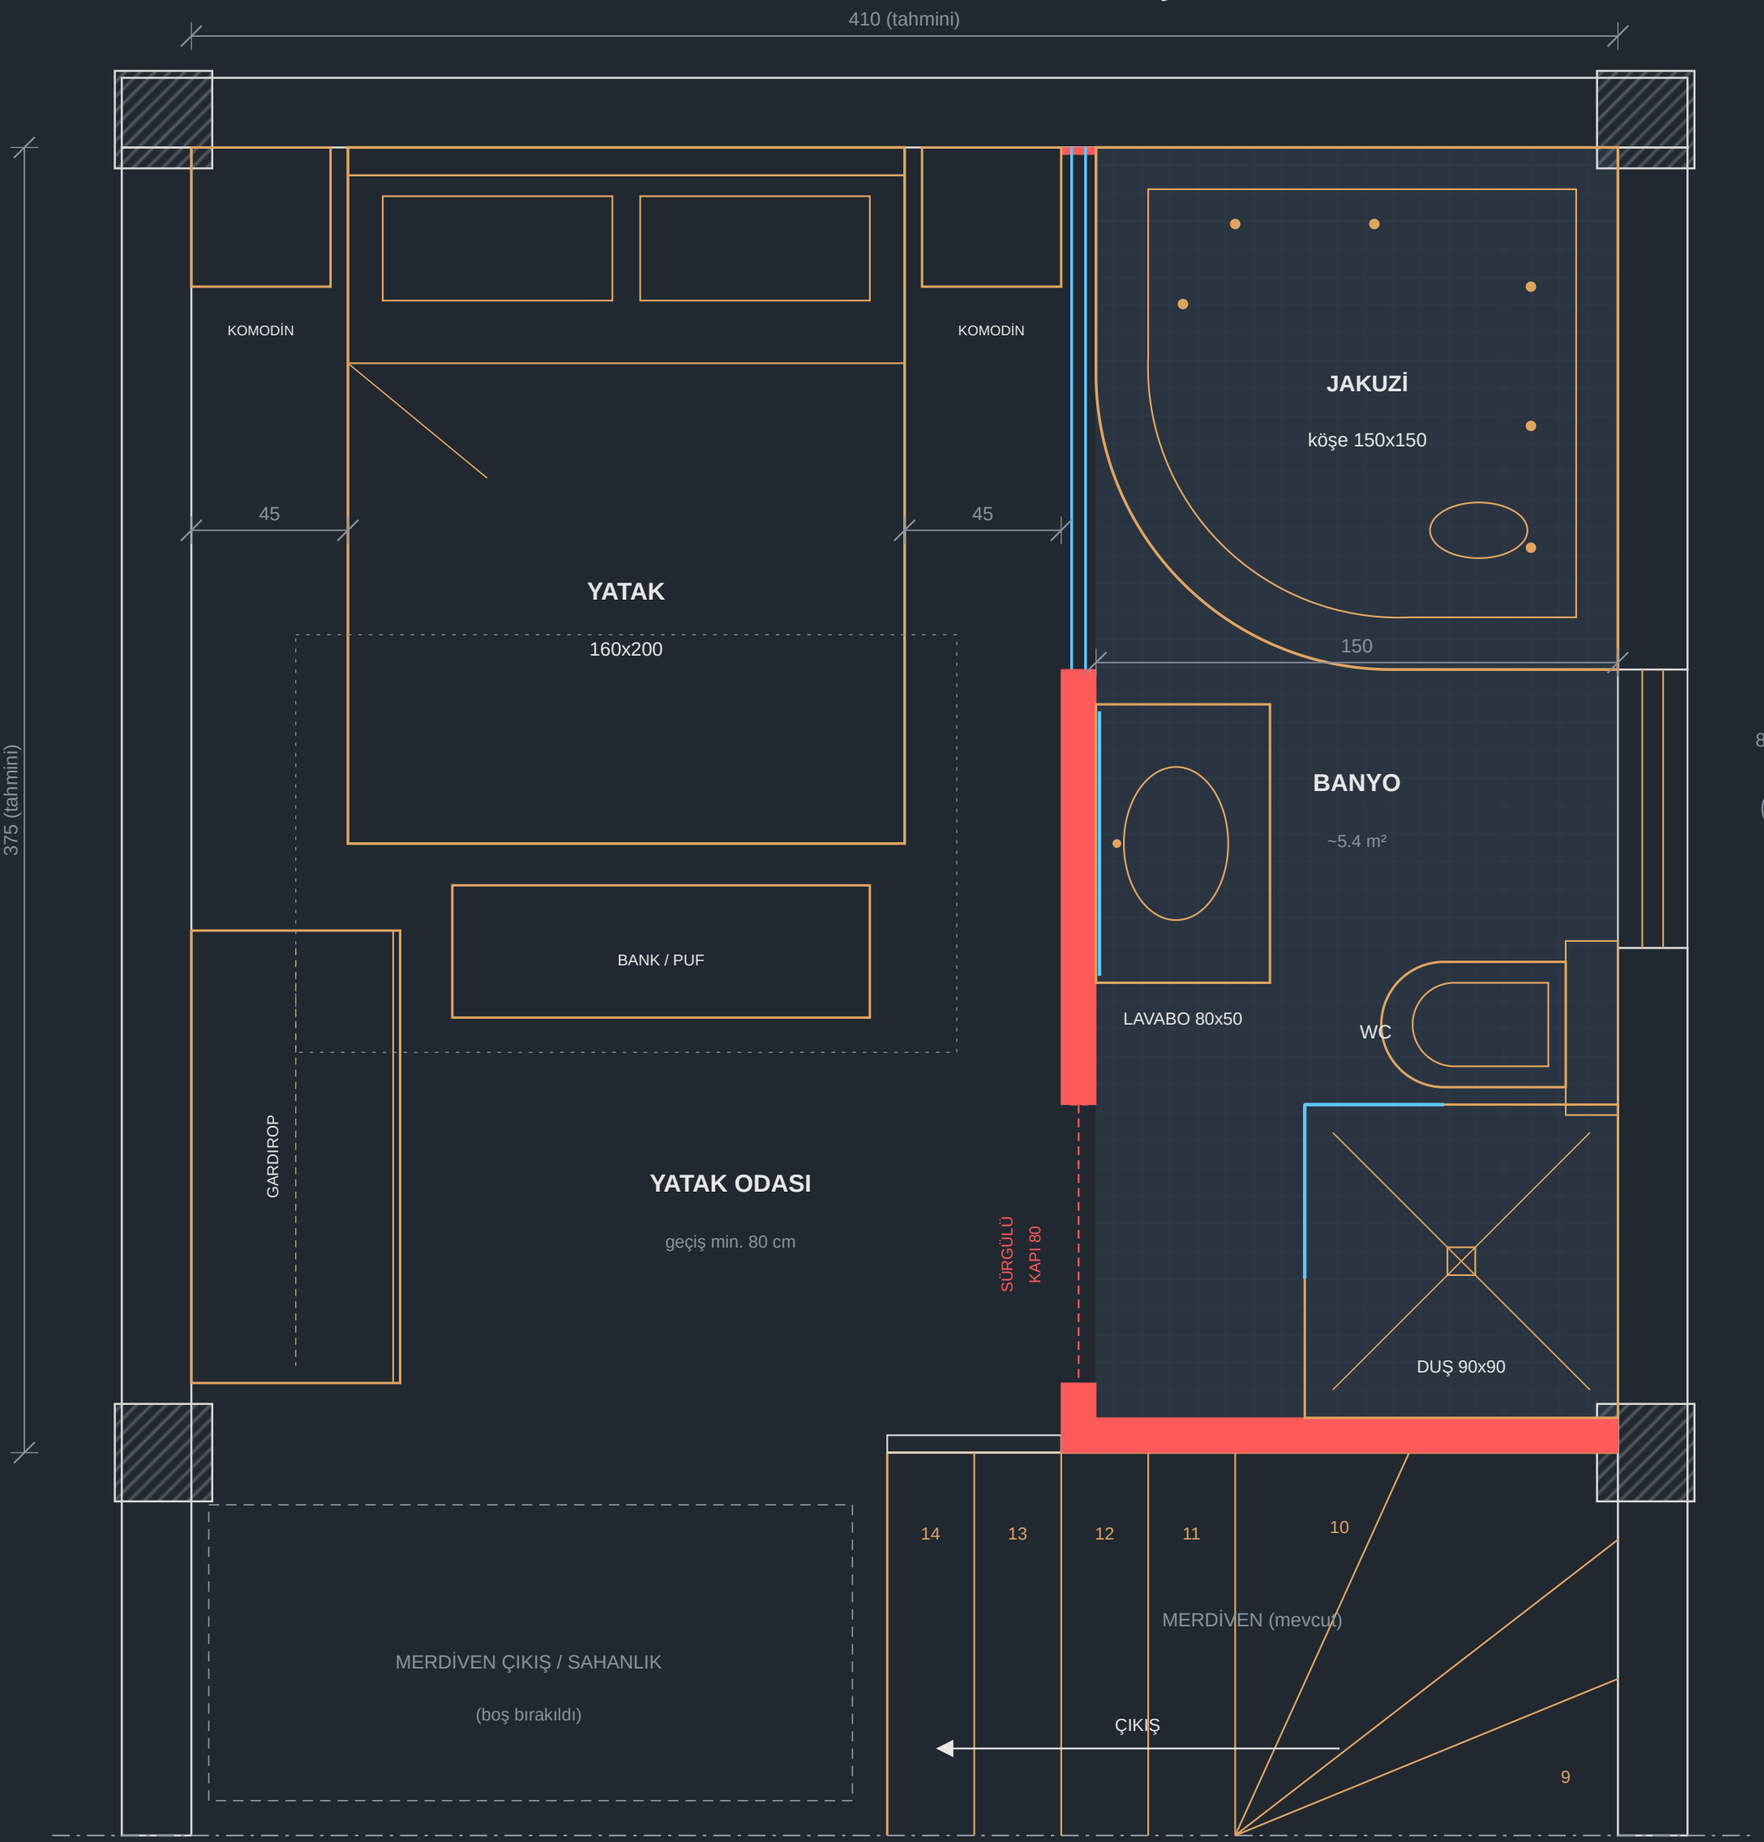

LEJANT

- Mevcut duvar / kolon
- Yeni bölme duvarı (10 cm)
- Cam bölme / duş camı / ayna
- Mobilya / vitrifiye
- Islak hacim (seramik)

NEDEN BU YERLEŞİM?


1. Tüm ıslak hacimler (jakuzi, duş, WC, lavabo) tek blokta, sağ şeritte → tesisat kısa, tek gider hattı, tek havalandırma.
2. Jakuzi sağ üst KÖŞEDE, kolonun dibinde. Dolu jakuzi ~500-600 kg → yük kolon/kirişe en yakın noktada. Statik kontrol şart.
3. Jakuzi ile yatak arası CAM bölme: yataktan jakuzi görünür (suit hissi). İstenirse buzlu / akıllı cam / perde.
4. P1 penceresi banyoda → doğal ışık + havalandırma; önü boş bırakıldı.
5. Merdiven çıkışı (sol alt) tamamen boş, banyo kapısına ve yatağa direkt geçiş.
6. Banyo kapısı sürgülü (cebe giren) → açılma alanı kaybı yok.
7. Yatak başı dış duvara (üst) dayalı, iki yanda 45 cm komodin + geçiş.

DİKKAT

- Ölçüler ekran görüntüsünden tahminidir (iç ~410 x 375). Net ölçüyle revize edilir.
- Jakuzi için ayrı sigortalı hat + topraklama.
- Islak hacimde su yalıtımı + 2 cm kot farkı.
- 180'lik yatak istenirse: sağ komodin kaldırılır, duvara asma raf konur.

plan aşağı doğru devam ediyor

LOFT KAT — ALTERNATİF 2: MANZARAYA BAKAN AÇIK JAKUZİ

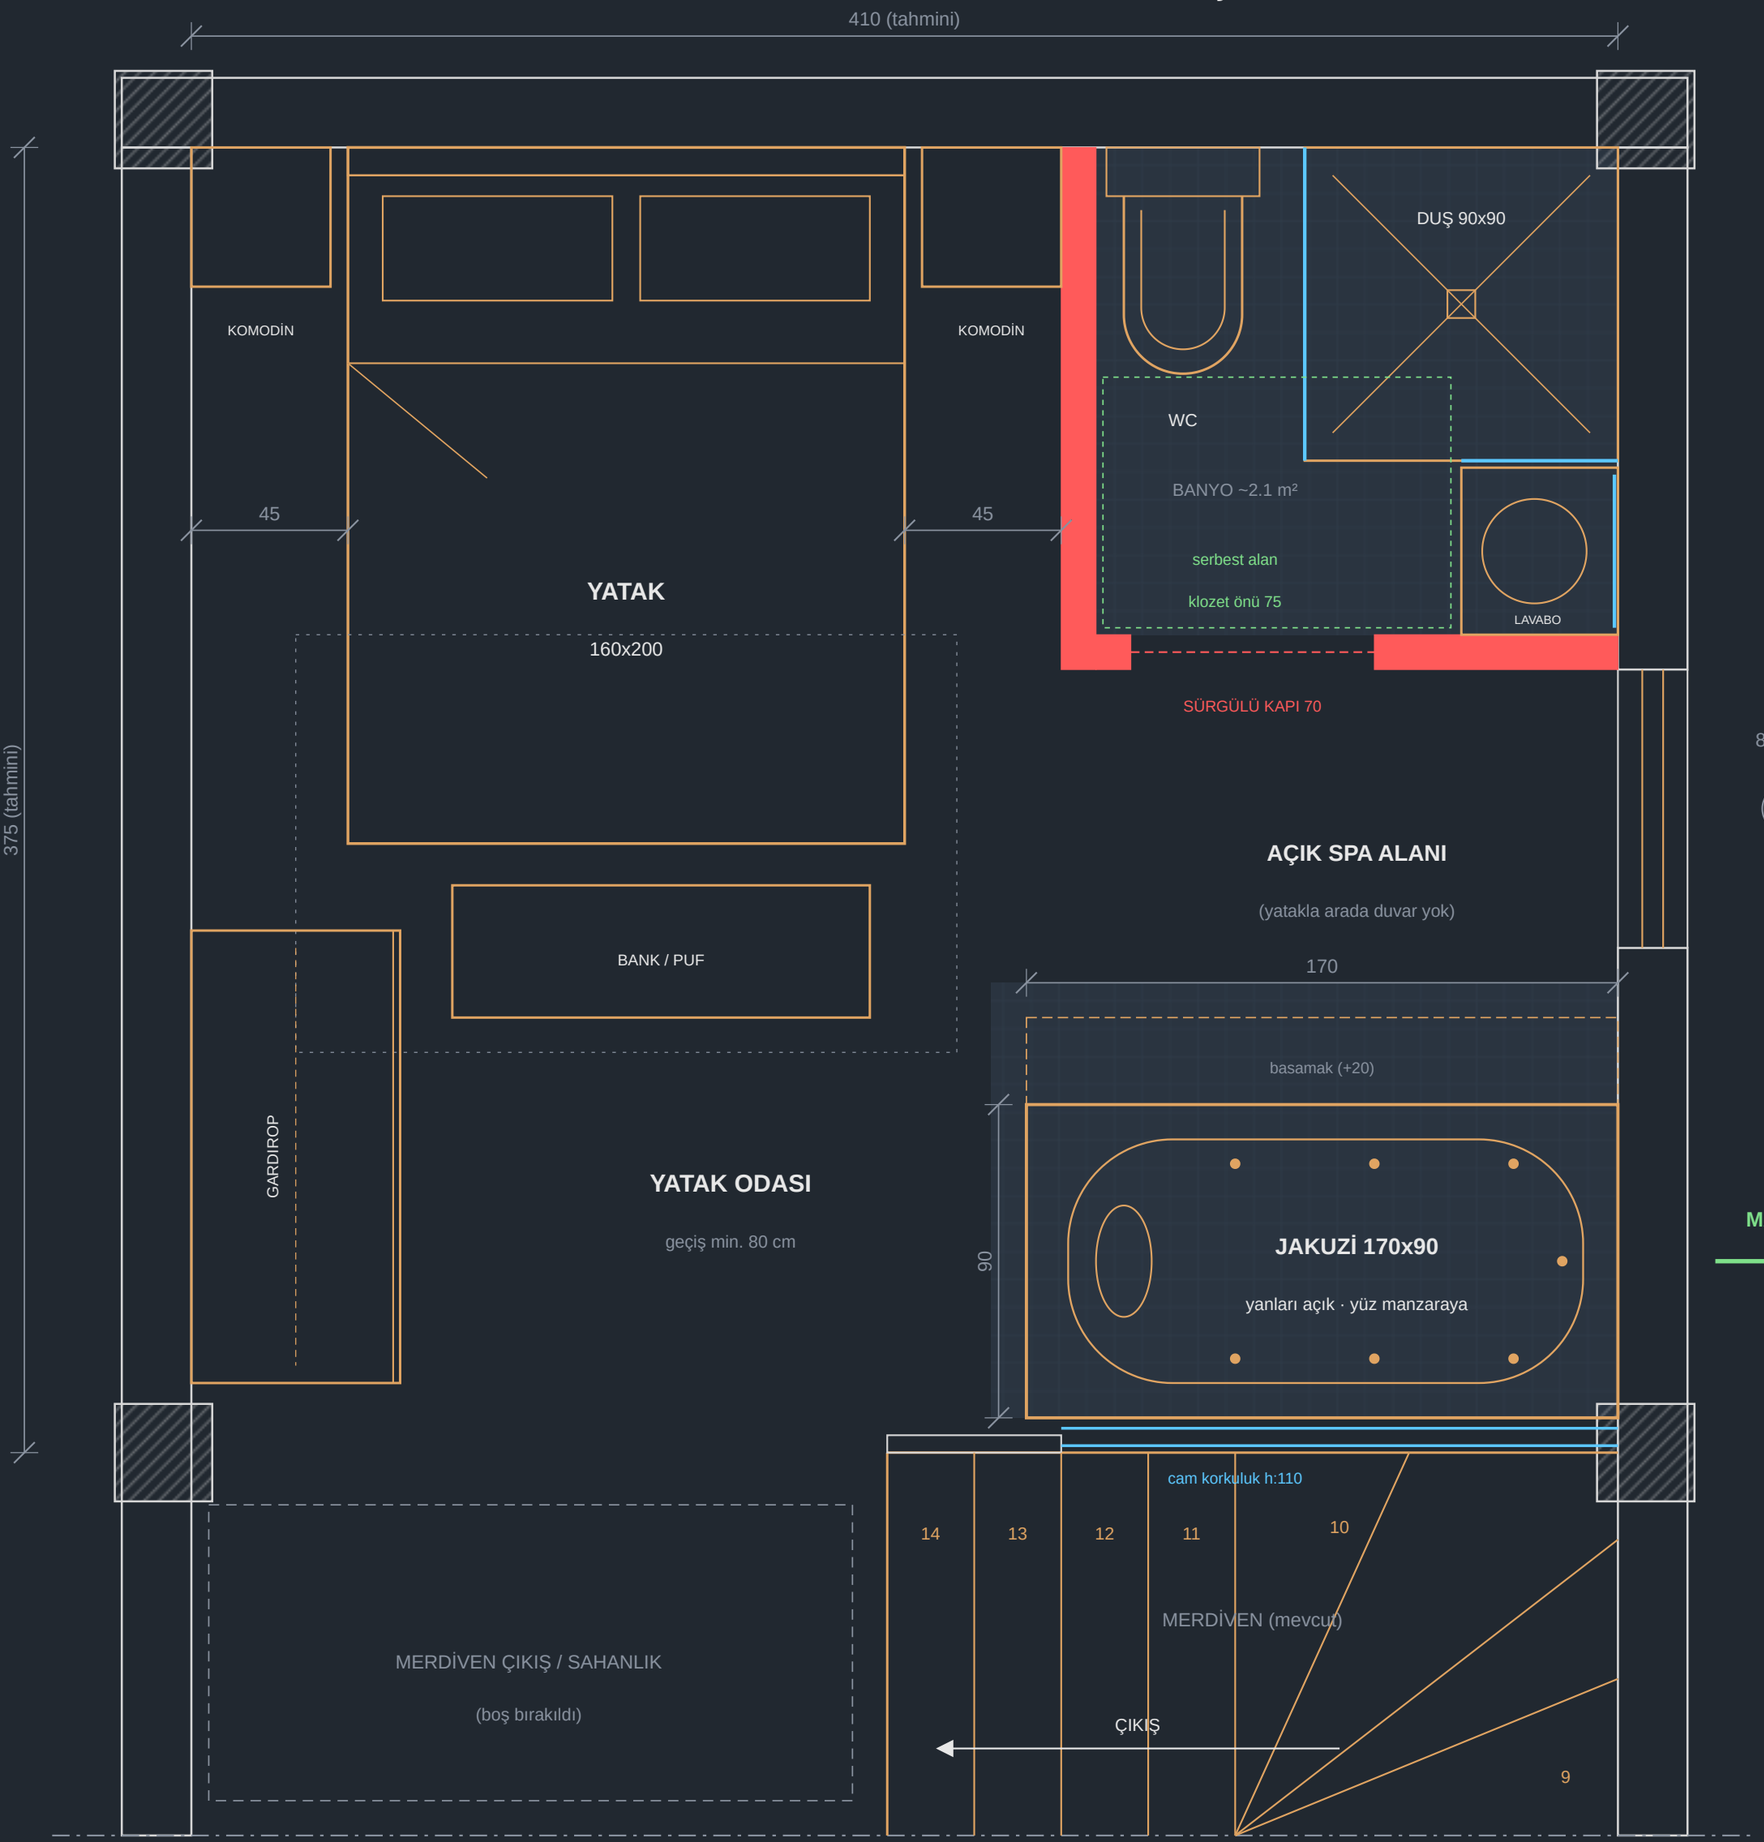

LEJANT

- Mevcut duvar / kolon
- Yeni bölme duvarı (10 cm)
- Cam korkuluk / duş camı / ayna
- Mobilya / vitrifiye
- Islak hacim (seramik)

BU VERSİYONDA NE DEĞİŞTİ?


1. Jakuzi, duşun olduğu yere (manzara tarafına) alındı. Başlık batıda → otururken yüzün direkt manzaraya.
2. Jakuzinin yanlarında duvar YOK: yatak + jakuzi + manzara tek mekân. Yataktan da manzara görünüyor.
3. Merdiven boşluğu tarafına duvar yerine CAM KORKULUK → güvenlik var, görüş açık.
4. WC + duş + lavabo sağ üst köşede küçük kapalı banyoda; jakuzi ile aynı tesisat hattında. Klozet önü 75 cm serbest.
5. P1 penceresinin önü boş, açık alanı aydınlatıyor. Merdiven çıkışı serbest.

DİKKAT

- Açık jakuzi buharı yatağa gelir: güçlü aspiratör / nem alma + jakuzi kapağı şart.
- Jakuzi çevresi ~1 m sıçrama alanı: seramik + su yalıtımı, parke ile arası şeritle ayrılır.
- Jakuzi merdiven boşluğu kenarında: dolu ~500-600 kg → kenar kirişi statik kontrol!
- Ölçüler ekran görüntüsünden tahminidir.

plan aşağı doğru devam ediyor

LOFT KAT — ALTERNATİF 4: JAKUZİ PENCERE ÖNÜNDE

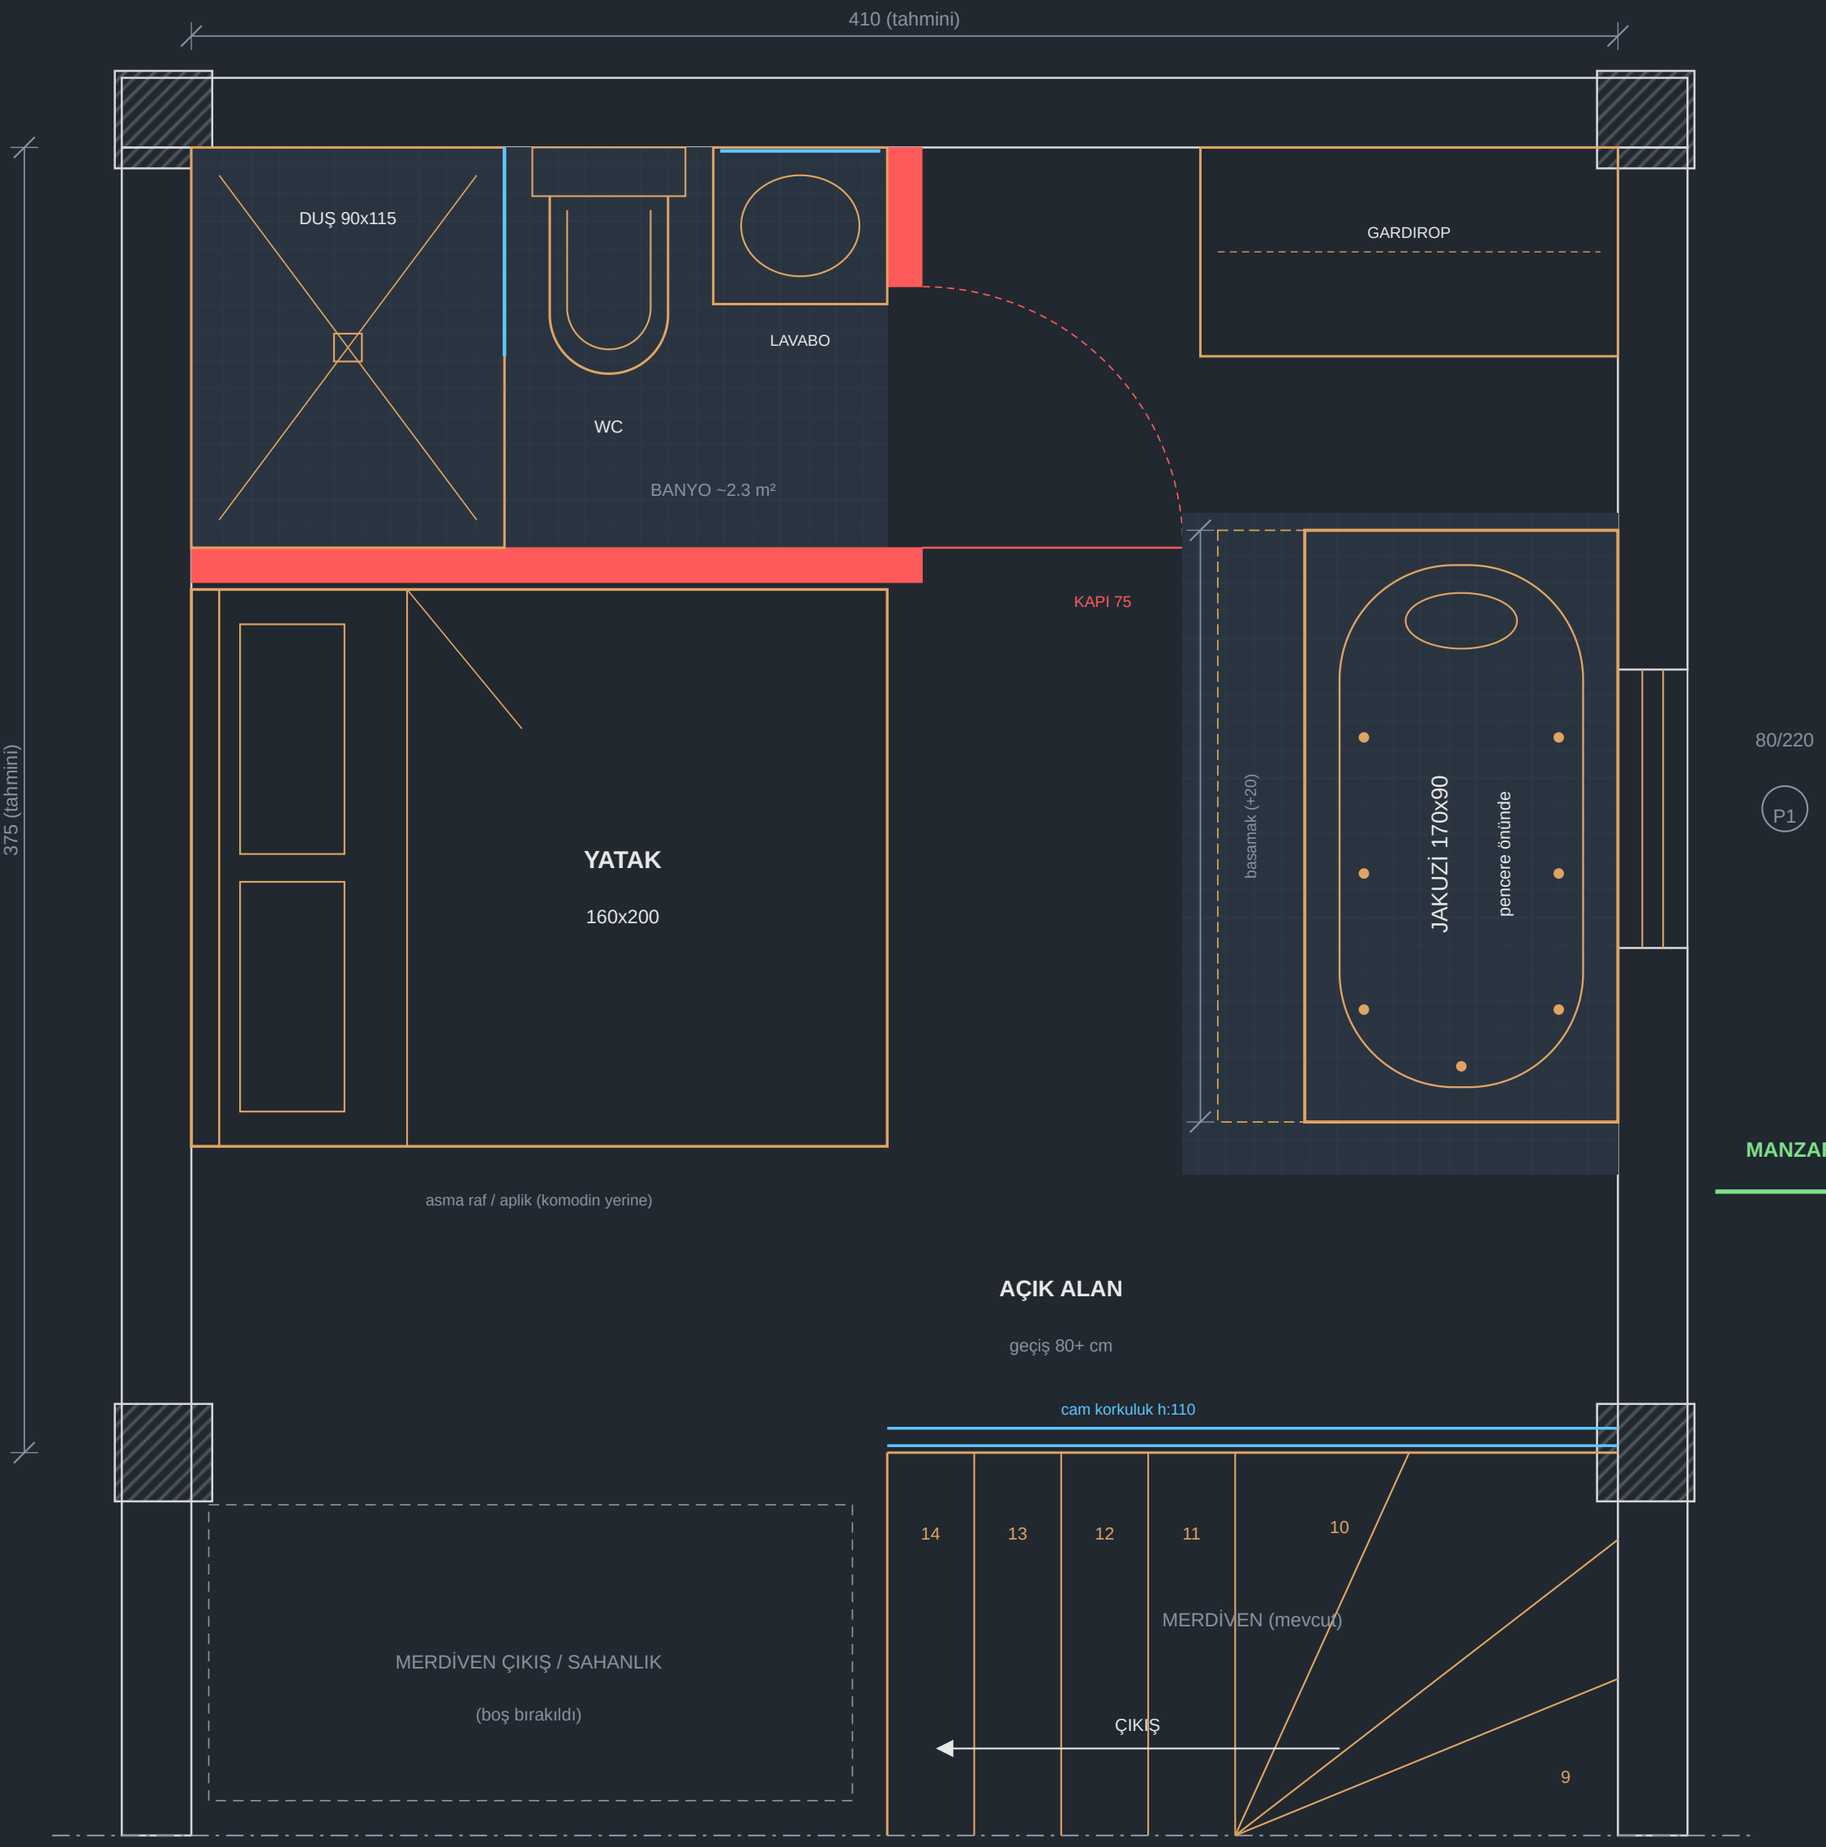

LEJANT

- Mevcut duvar / kolon
- Yeni bölme duvarı (10 cm) / kapı
- Cam / korkuluk / ayna
- Mobilya / vitrifiye
- Islak hacim (seramik)


ALTERNATİF 4 — FİKİR

1. Jakuzi tam P1 penceresinin önünde: yatarken yanında boydan pencere.
2. Banyo üst duvar boyunca (duş, WC, lavabo yan yana), kapı sağa açılır.
3. Yatak sol duvarda NİŞ gibi: ayak ucu jakuziye ve pencereye bakıyor.
4. Gardırop sağ üst köşede, jakuzinin arkasında; sağ alt köşe tamamen boş.
5. Merdiven çıkışından her yere 80+ cm.

DİKKAT

- Yatak bir uzun kenarıyla banyo duvarına dayalı → tek taraftan inilir, komodin yok.
- Jakuzi pencereyi kapatır: P1 kapı/Fransız balkon ise kullanılamaz, sadece manzara.
- Banyo dar (~2.3 m²) ama 3 parça sığıyor.
- Açık jakuzi: aspiratör / nem alma şart.

LOFT KAT — ALTERNATİF 5: KAPALI SPA BANYO

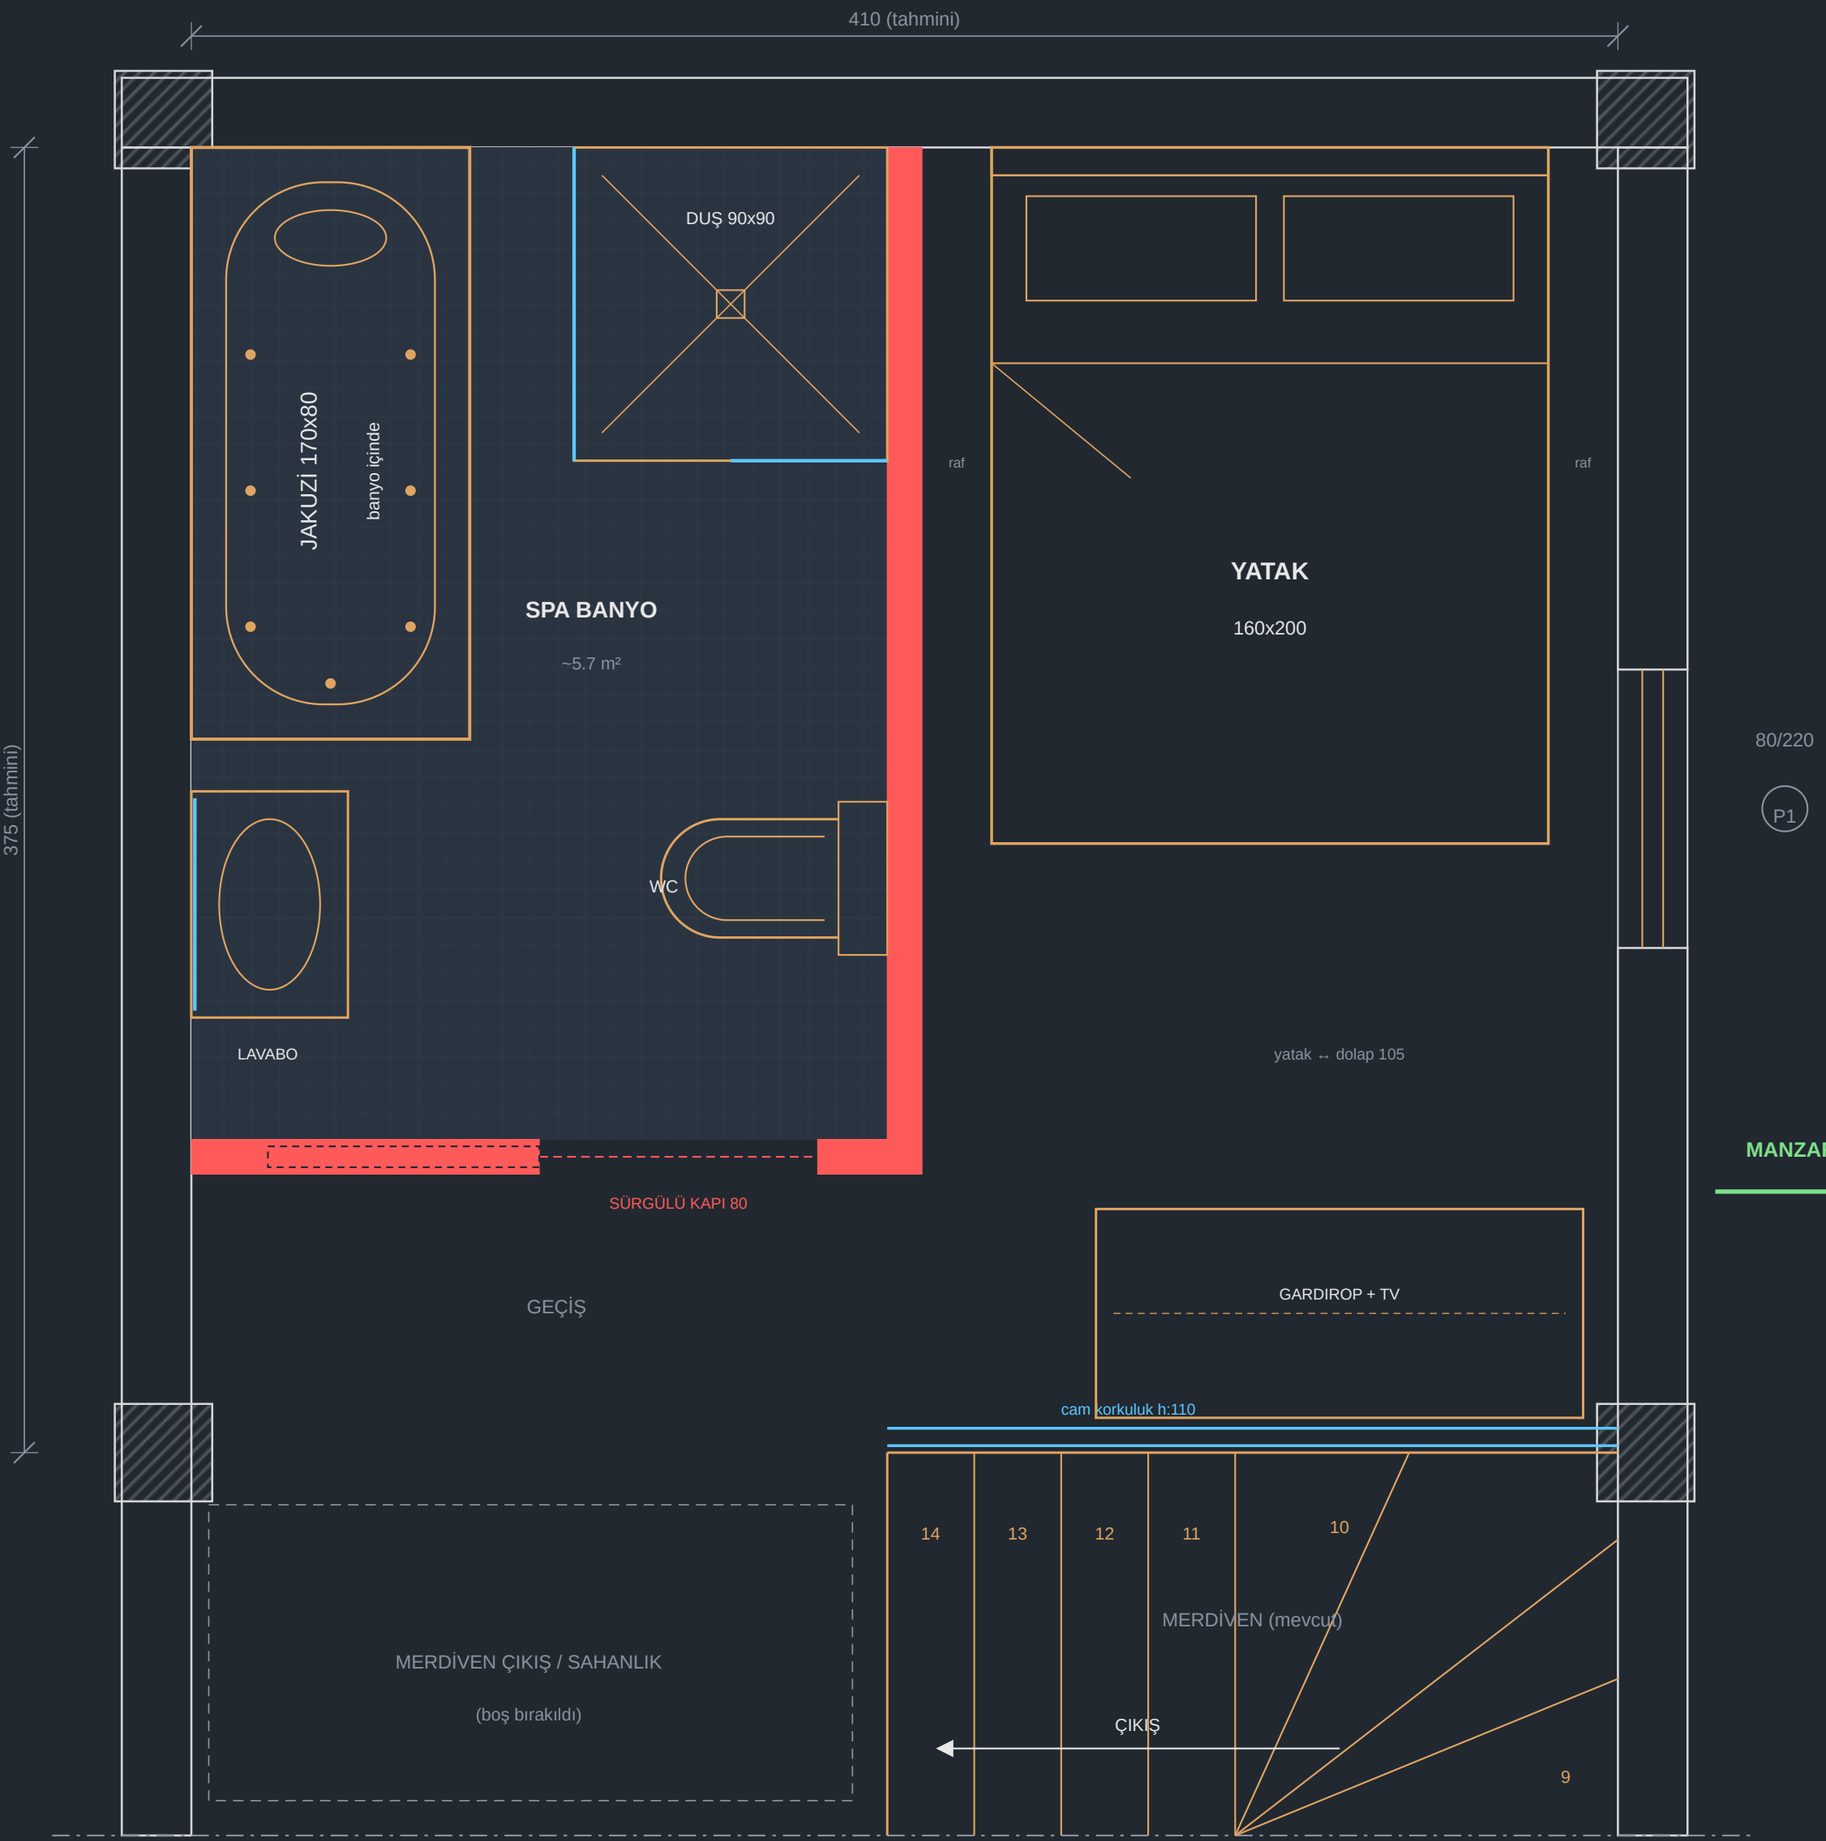

LEJANT

- Mevcut duvar / kolon
- Yeni bölme duvarı (10 cm) / kapı
- Cam / korkuluk / ayna
- Mobilya / vitrifiye
- Islak hacim (seramik)

ALTERNATİF 5 — FİKİR

1. Jakuzi, duş, WC, lavabo hepsi tek büyük KAPALI spa banyoda (~5.7 m²).
2. Buhar / nem / ses yatağa geçmez, yatak odası tamamen kuru kalır.
3. Yatak sağda, P1 penceresinin yanında; karşısında gardırop + TV duvarı.
4. Tüm tesisat sol dış duvar boyunca, tek gider hattı → en ucuz çözüm.
5. Merdivenden çıkınca banyo kapısı ve yatak odası ayrı ayrı erişilir.

DİKKAT

- Jakuzide manzara YOK (iç tarafta).
- Yatağın iki yanında sadece 20 cm: komodin yerine duvara asma raf.
- Jakuzi dolu ~400 kg: sol dış duvar boyunca, statik açıdan en güvenli yer.

plan aşağı doğru devam ediyor